1：15,000 地形図

尾張都市計画区域

小牧市区画整理総括図

（計　画　道　路）	愛知県告示	第１３０号	令和 ２年 ３月27日
	小牧市告示	第　５２号	令和 ２年 ３月27日
（市 街 化 区 域）	愛知県告示	第１６０号	令和 ７年 ３月25日
（用　途　地　域）	小牧市告示	第　３８号	令和 ７年 ３月25日
（防火・準防火地域）	小牧市告示	第１０７号	平成22年12月24日
（地　区　計　画）	小牧市告示	第110,114,115号	平成22年12月24日
	小牧市告示	第 43～46号	平成29年 ４月 １日
	小牧市告示	第 41,42号	平成30年 ４月 １日
	小牧市告示	第　２３号	令和 ３年 ３月17日
	小牧市告示	第１１１号	令和 ５年10月 １日
	小牧市告示	第　３９号	令和 ７年 ３月25日
（駐車場整備地区）	小牧市告示	第１０８号	平成22年12月24日
（高度利用地区）	小牧市告示	第１０６号	平成22年12月24日

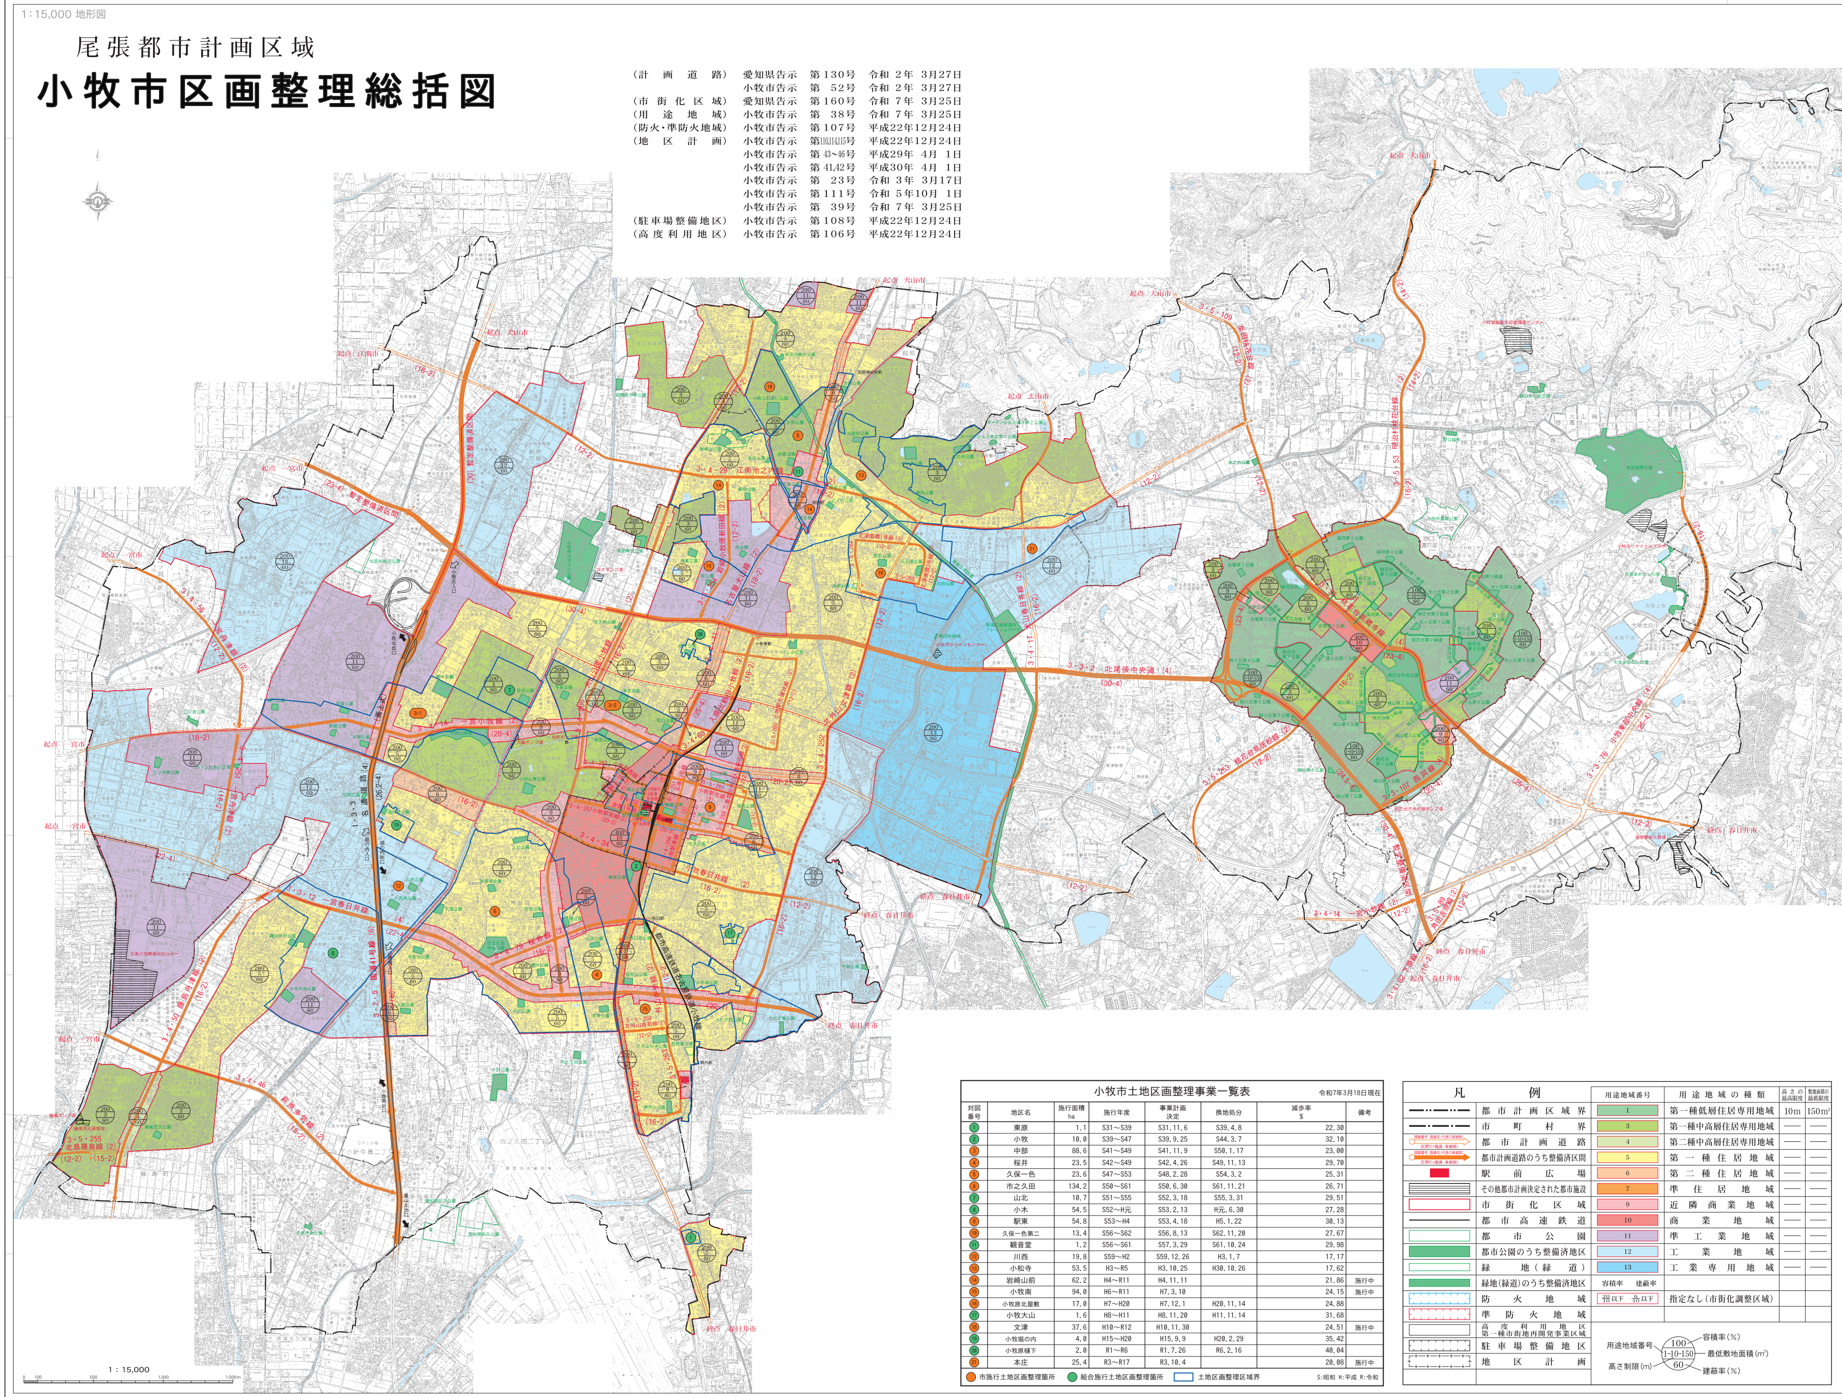

1 : 15,000

小牧市土地区画整理事業一覧表

令和7年3月18日現在

対図番号	地区名	施行面積 ha	施行年度	事業計画決定	換地処分	減歩率 %	備考
①	東原	1.1	S31～S39	S31.11.6	S39.4.8	22.30	
②	小牧	10.0	S39～S47	S39.9.25	S44.3.7	32.10	
③	中部	88.6	S41～S49	S41.11.9	S50.1.17	23.00	
④	桜井	23.5	S42～S49	S42.4.26	S49.11.13	29.70	
⑤	久保一色	23.6	S47～S53	S48.2.28	S54.3.2	25.31	
⑥	市之久田	134.2	S50～S61	S50.6.30	S61.11.21	26.71	
⑦	山北	10.7	S51～S55	S52.3.18	S55.3.31	29.51	
⑧	小木	54.5	S52～H元	S53.2.13	H元.6.30	27.28	
⑨	駅東	54.8	S53～H4	S53.4.18	H5.1.22	30.13	
⑩	久保一色第二	13.4	S56～S62	S56.8.13	S62.11.20	27.67	
⑪	観音堂	1.2	S56～S61	S57.3.29	S61.10.24	29.98	
⑫	川西	19.8	S59～H2	S59.12.26	H3.1.7	17.17	
⑬	小松寺	53.5	H3～R5	H3.10.25	H30.10.26	17.62	
⑭	岩崎山前	62.2	H4～R11	H4.11.11		21.86	施行中
⑮	小牧南	94.0	H6～R11	H7.3.10		24.15	施行中
⑯	小牧原北屋敷	17.0	H7～H20	H7.12.1	H20.11.14	24.88	
⑰	小牧大山	1.6	H8～H11	H8.11.20	H11.11.14	31.68	
⑱	文津	37.6	H10～R12	H10.11.30		24.51	施行中
⑲	小牧堀の内	4.0	H15～H20	H15.9.9	H20.2.29	35.42	
⑳	小牧原樋下	2.0	R1～R6	R1.7.26	R6.2.16	40.04	
㉑	本庄	25.4	R3～R17	R3.10.4		20.08	施行中

● 市施行土地区画整理箇所　● 組合施行土地区画整理箇所　□ 土地区画整理区域界　S:昭和 H:平成 R:令和

凡例		用途地域番号	用途地域の種類	高さの最高限度	敷地面積の最低限度
—··—··—	都市計画区域界	1	第一種低層住居専用地域	10m	150m²
—·—·—	市町村界	3	第一種中高層住居専用地域	——	——
路線番号 路線名(代表の車線数) 区間の(幅員・車線数)	都市計画道路	4	第二種中高層住居専用地域	——	——
路線番号 路線名(代表の車線数) 区間の(幅員・車線数)	都市計画道路のうち整備済区間	5	第一種住居地域	——	——
🟥	駅前広場	6	第二種住居地域	——	——
▤	その他都市計画決定された都市施設	7	準住居地域	——	——
□	市街化区域	9	近隣商業地域	——	——
—	都市高速鉄道	10	商業地域	——	——
□	都市公園	11	準工業地域	——	——
🟩	都市公園のうち整備済地区	12	工業地域	——	——
□	緑地（緑道）	13	工業専用地域	——	——
🟩	緑地(緑道)のうち整備済地区	容積率　建蔽率			
⊡	防火地域	$\frac{20}{10}$以下　$\frac{6}{10}$以下	指定なし（市街化調整区域）		
⊡	準防火地域				
□	高度利用地区 第一種市街地再開発事業区域				
⊡	駐車場整備地区				
⊡	地区計画				

用途地域番号　100　容積率（%）
1-10-150　最低敷地面積（m²）
高さ制限（m）　60　建蔽率（%）

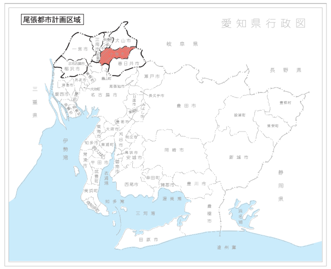

尾張都市計画区域

愛知県行政図

「この地図は、国土交通省国土地理院長の承認（平16 部公第56号）を得て、1:2500 小牧都市計画基本図を縮小、編集トレースしたものである。」

「この測量成果は、国土地理院長の承認及び助言を得て同院所管の測量標及び測量成果を使用して得たものである。（承認番号） 平16 部公 第56 号」

「この測量成果は、国土地理院長の承認及び助言を得て同院所管の測量標及び測量成果を使用して得たものである。（承認番号） 平21 部公 第170 号」

「この測量成果は、国土地理院長の助言を受けて得たものである。（助言番号） 平26 部公 第236号」

「この測量成果は、国土地理院長の助言を受けて得たものである。（助言番号） 令 1 部公 第134 号」

「この測量成果は、国土地理院長の助言を受けて得たものである。（助言番号） 令 7 部公 第 59 号」

小牧市役所

※この図面は、都市計画の概ねの位置・区域を表示したものであり、
詳細については計画図で確認して下さい。

令和8年３月印刷